



Узлы стеновых панелей. Complanar 50 - Наличник Shade.


J
Теневая коробка Complanar
Открытие наружу
Конфигурация проема. Тип 1

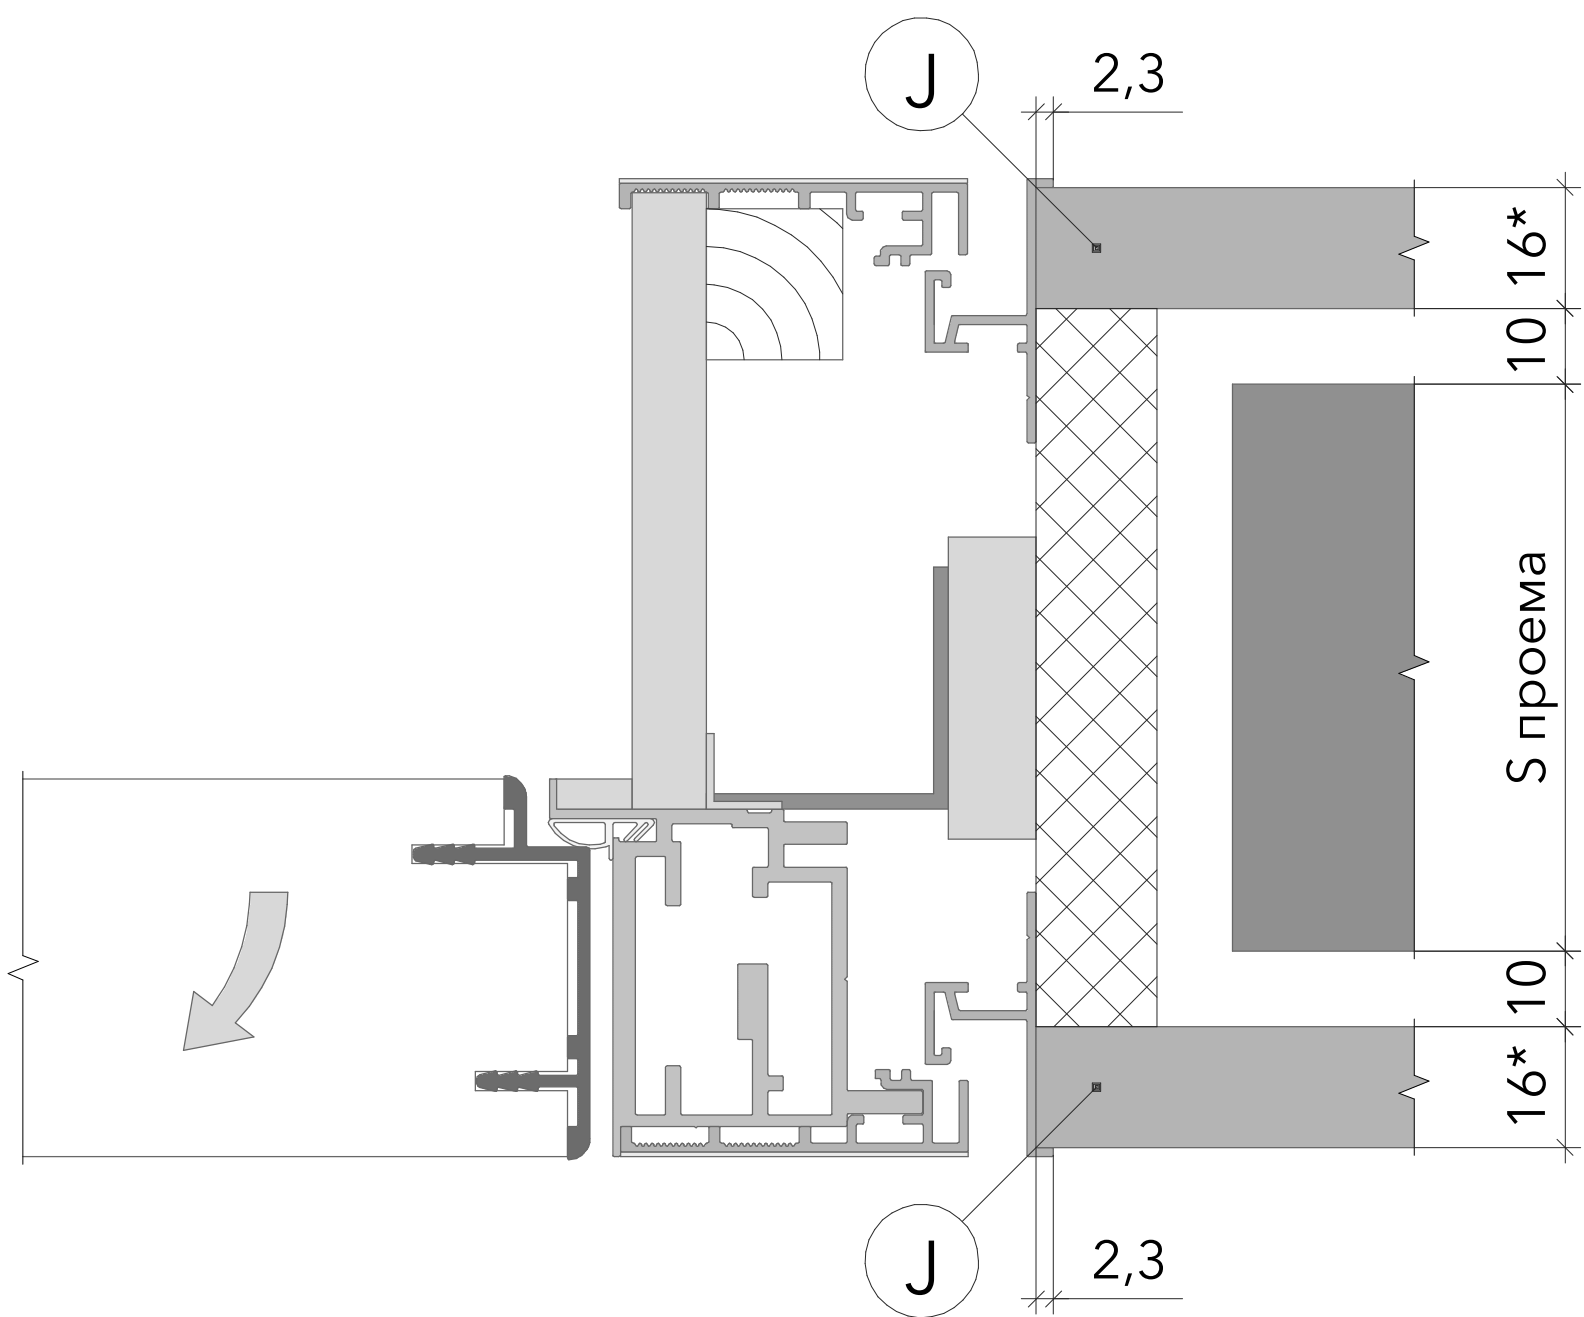


J
Теневая коробка Complanar
Открытие наружу
Конфигурация проема. Тип 2

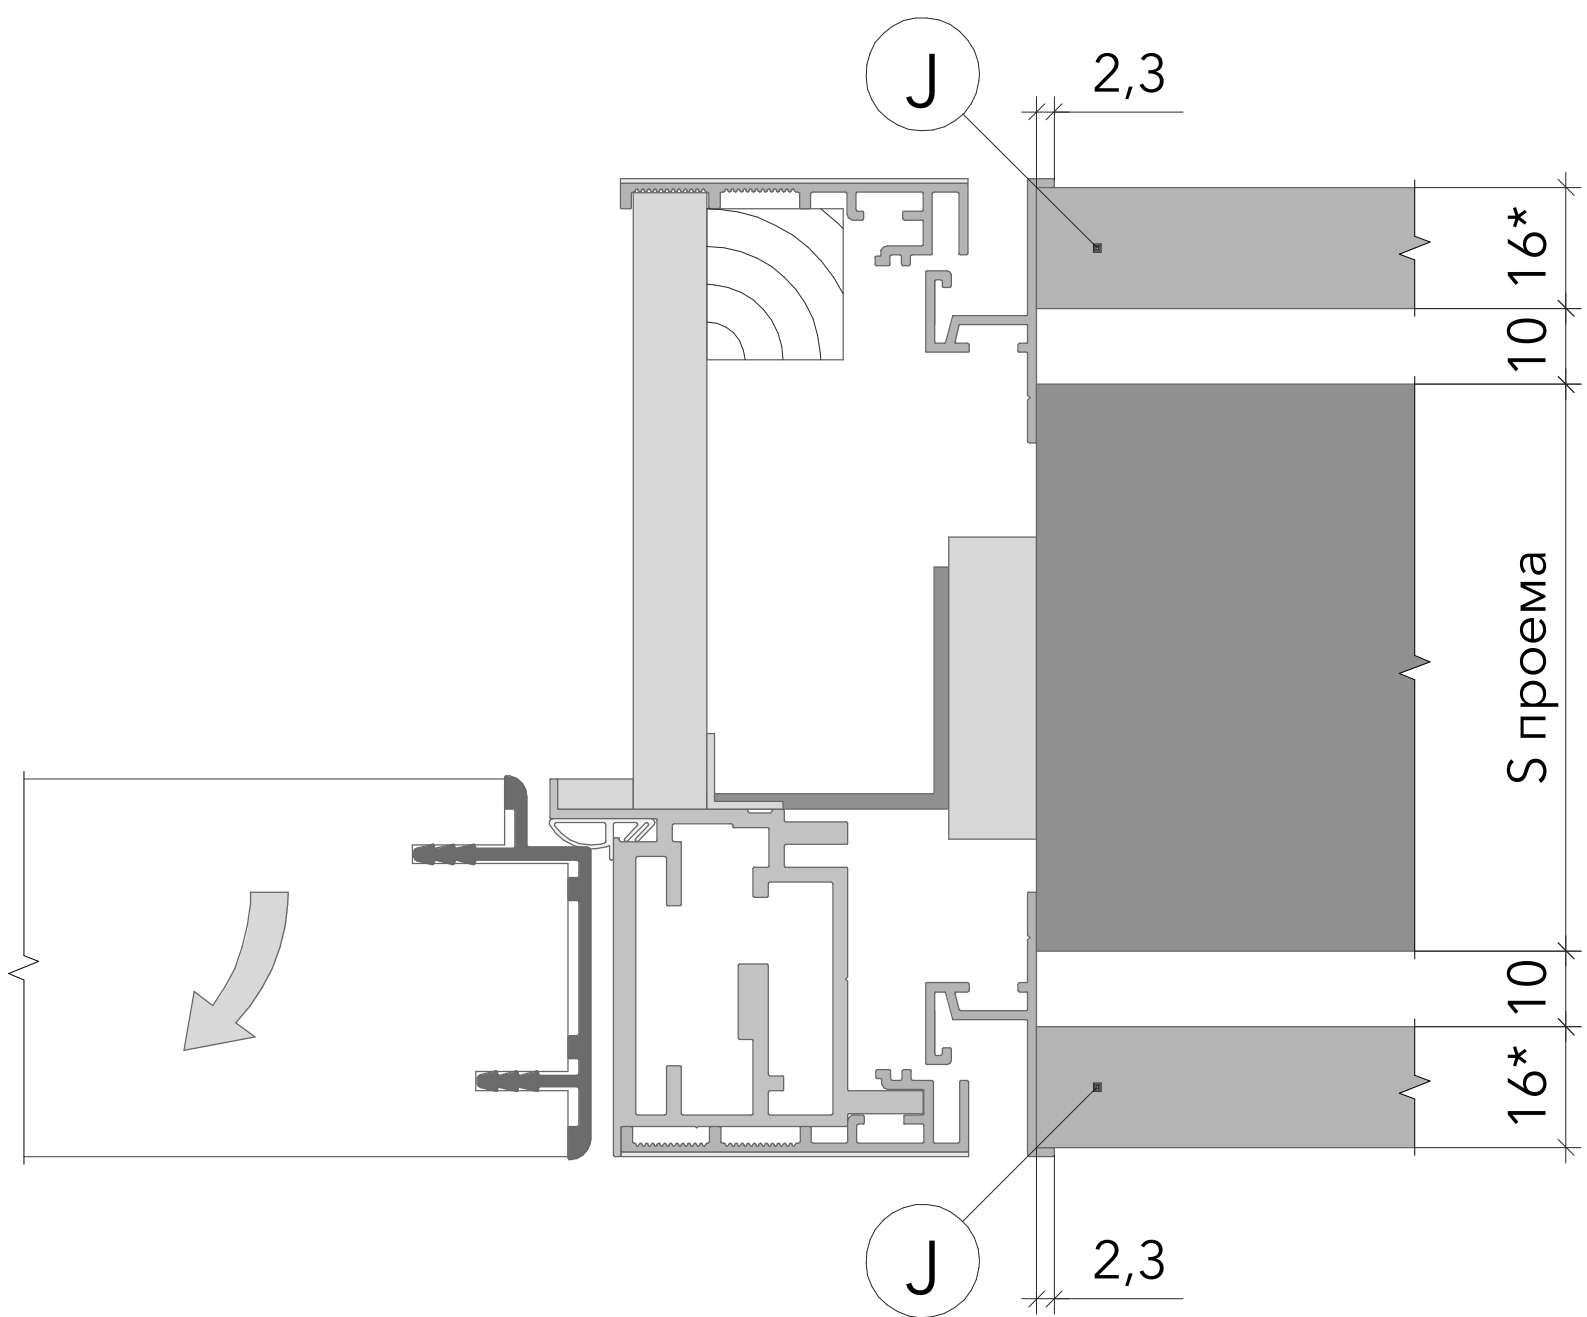


Коробка Complanar 50
Наличник Shade
Открытие наружу

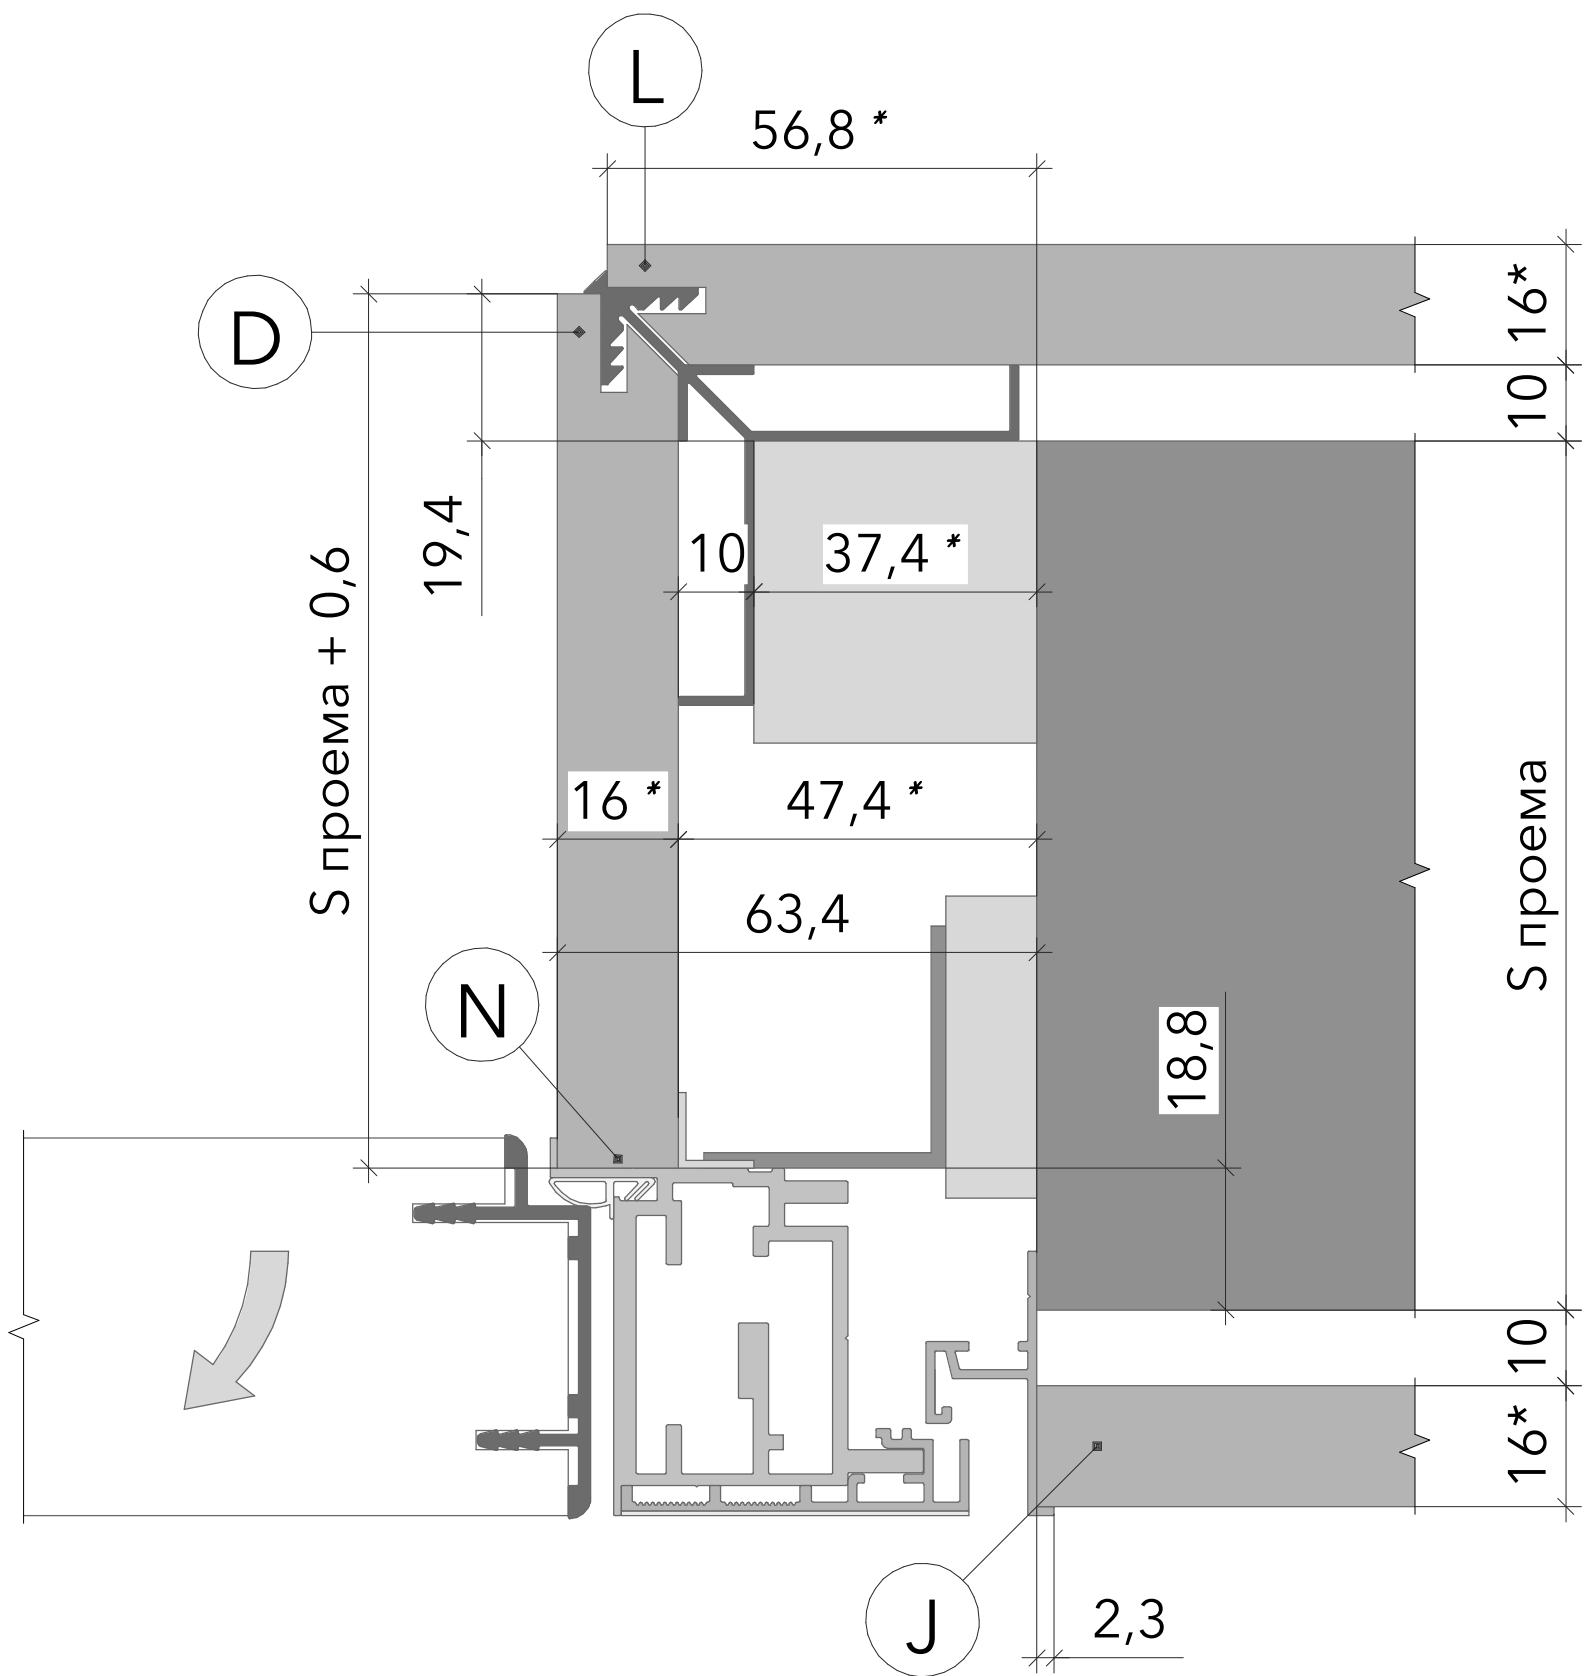


K
Теневой плинтус

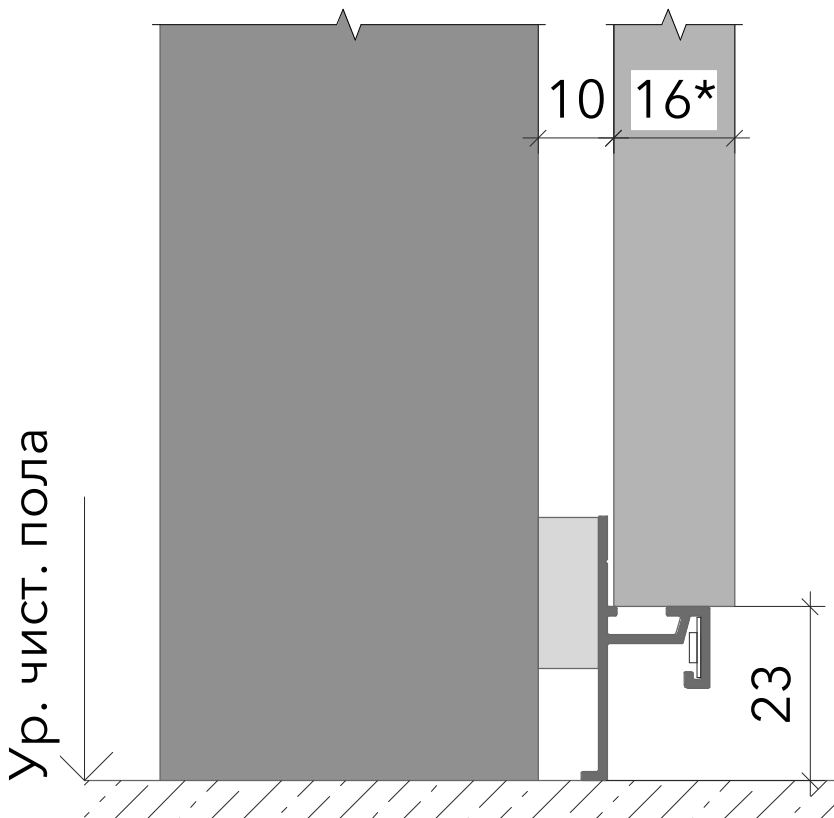


J
Теневая коробка Complanar
Открытие внутрь
Конфигурация проема. Тип 1

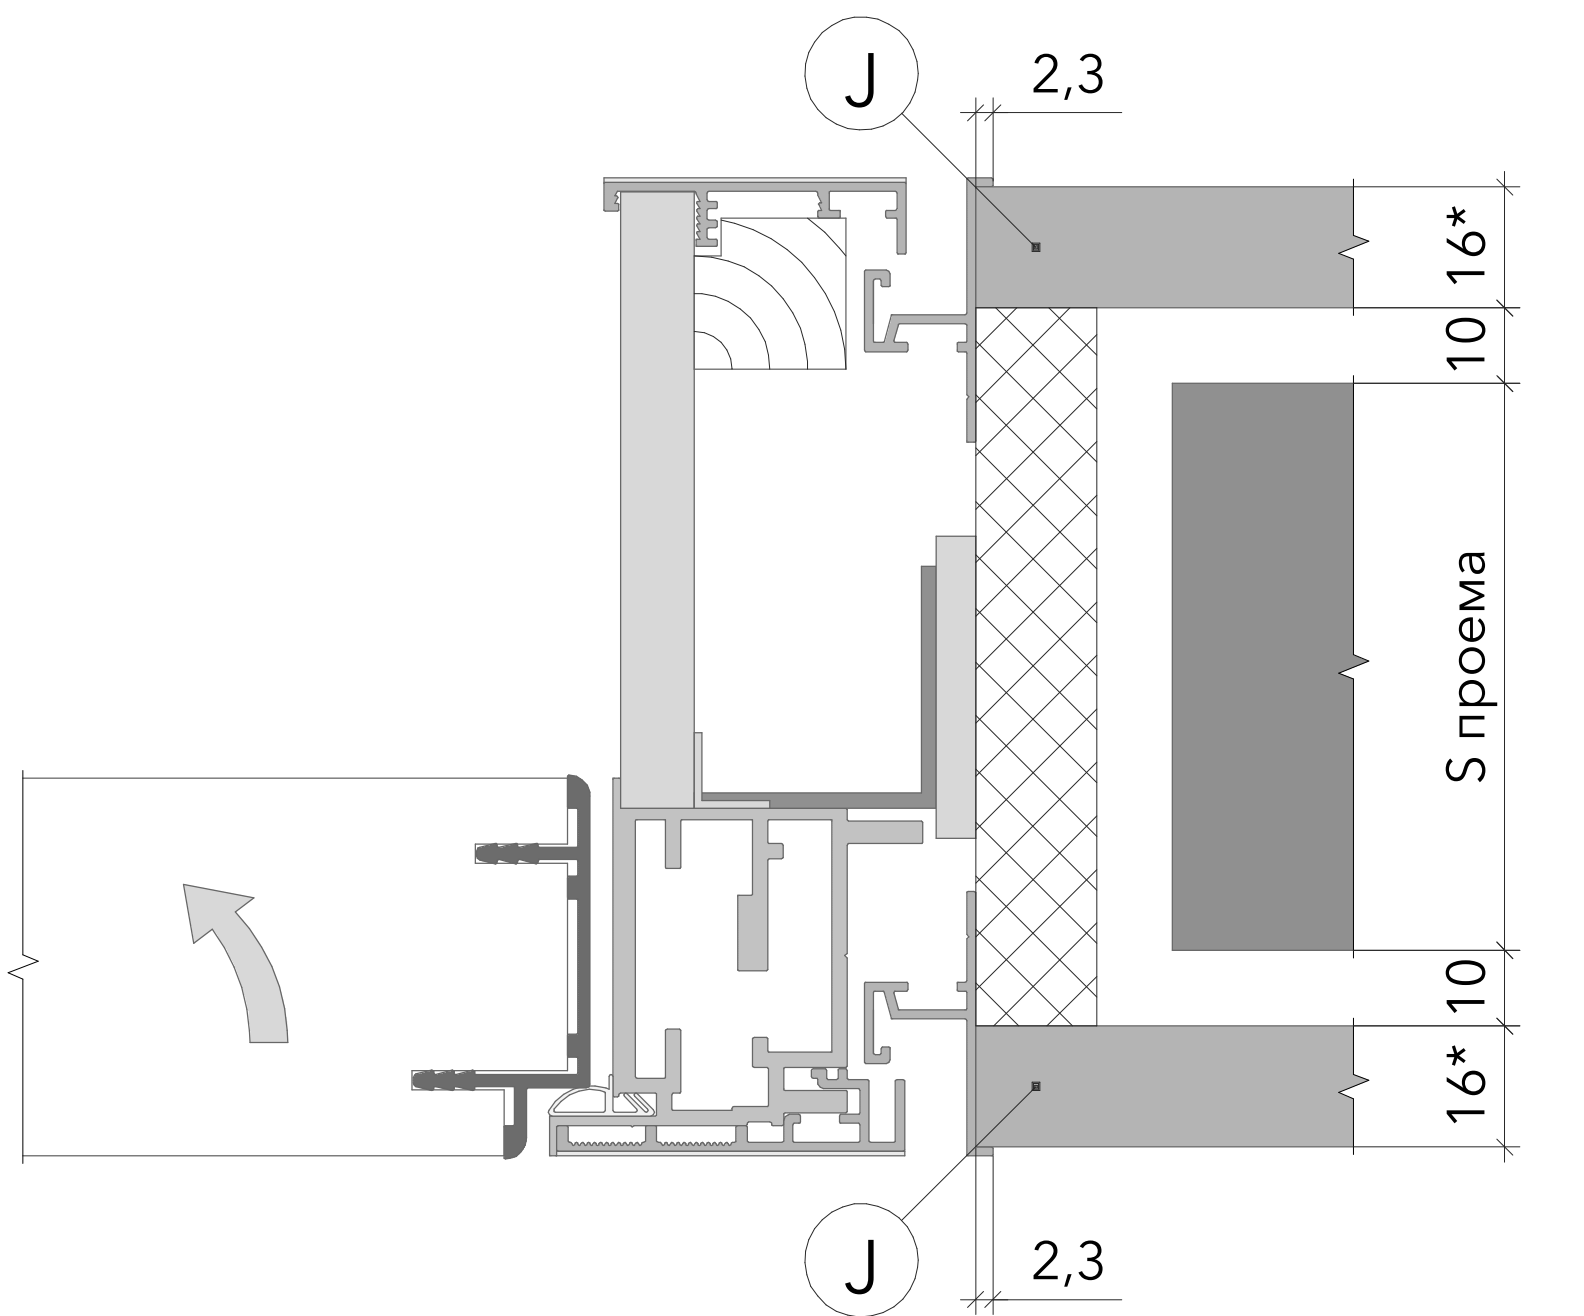

J
Теневая коробка Complanar
Открытие внутрь
Конфигурация проема. Тип 2

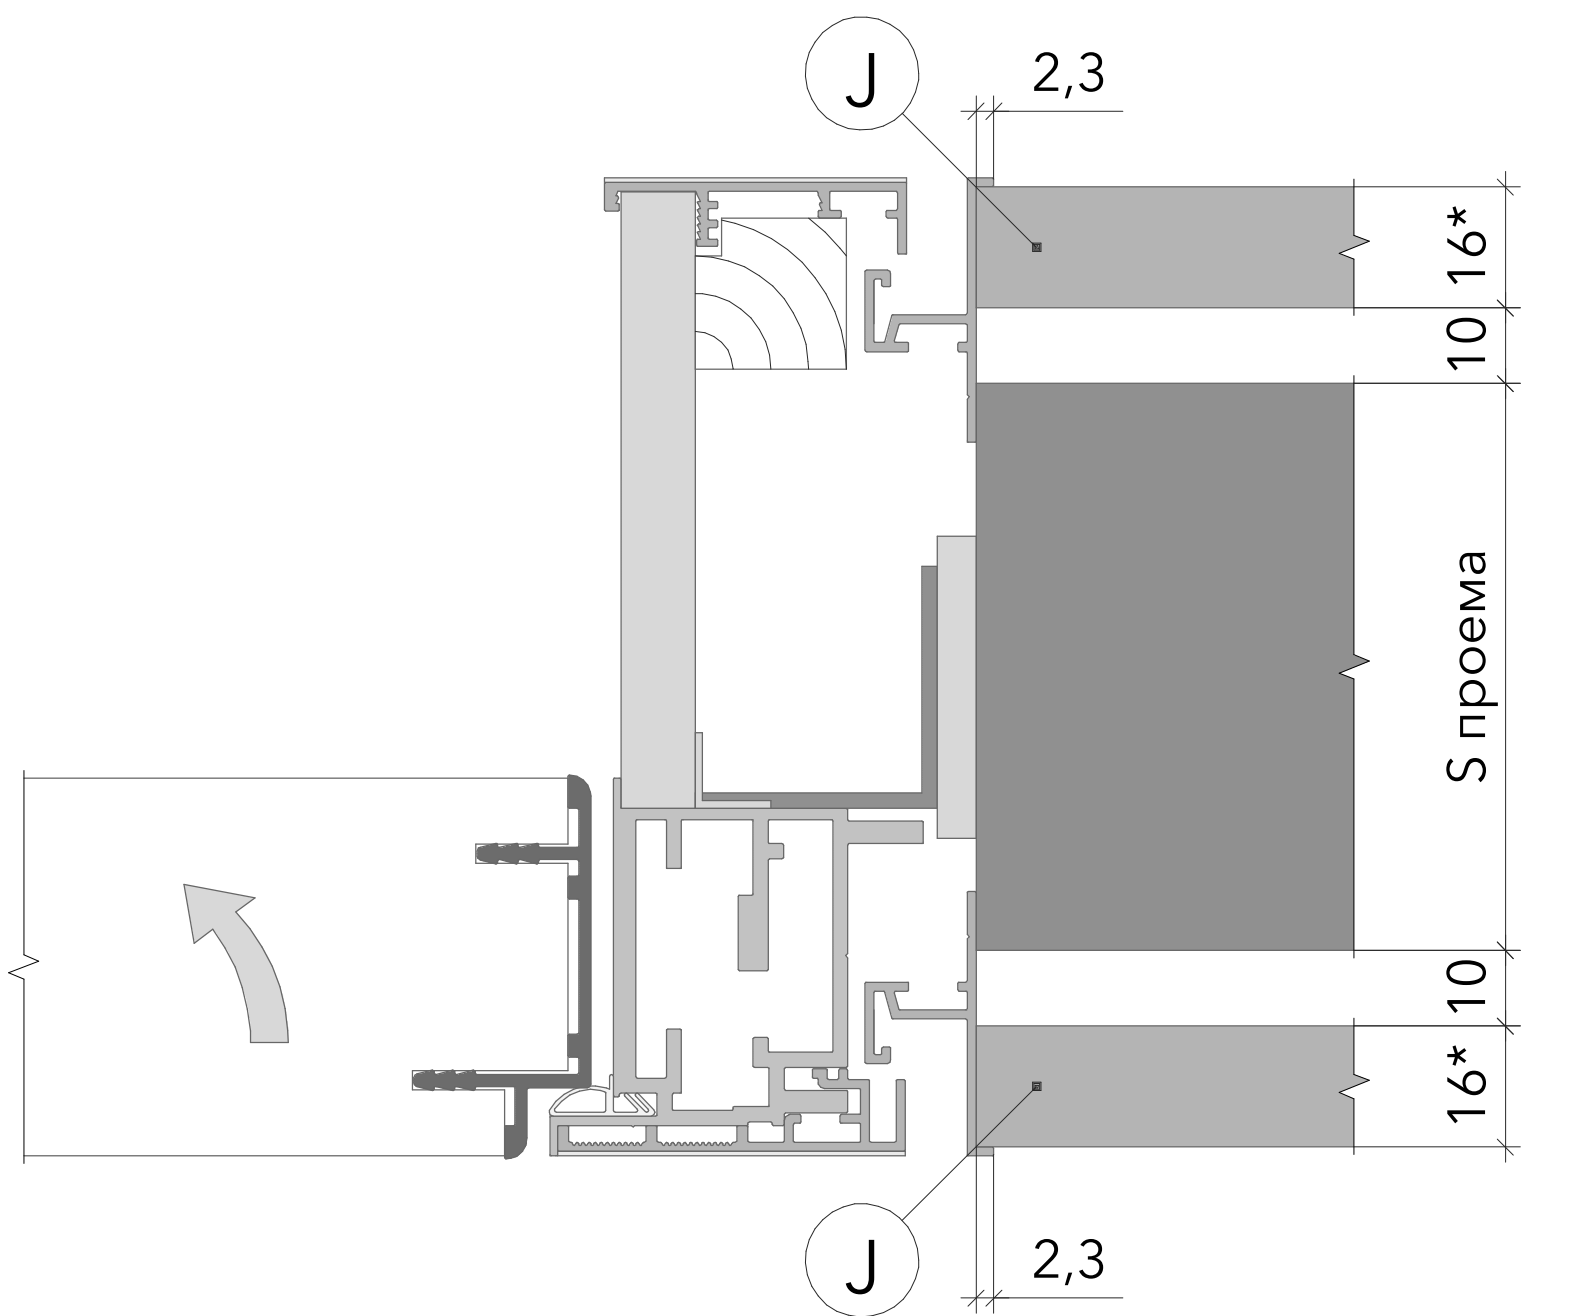

Коробка Complanar 50
Наличник Shade
Открытие внутрь

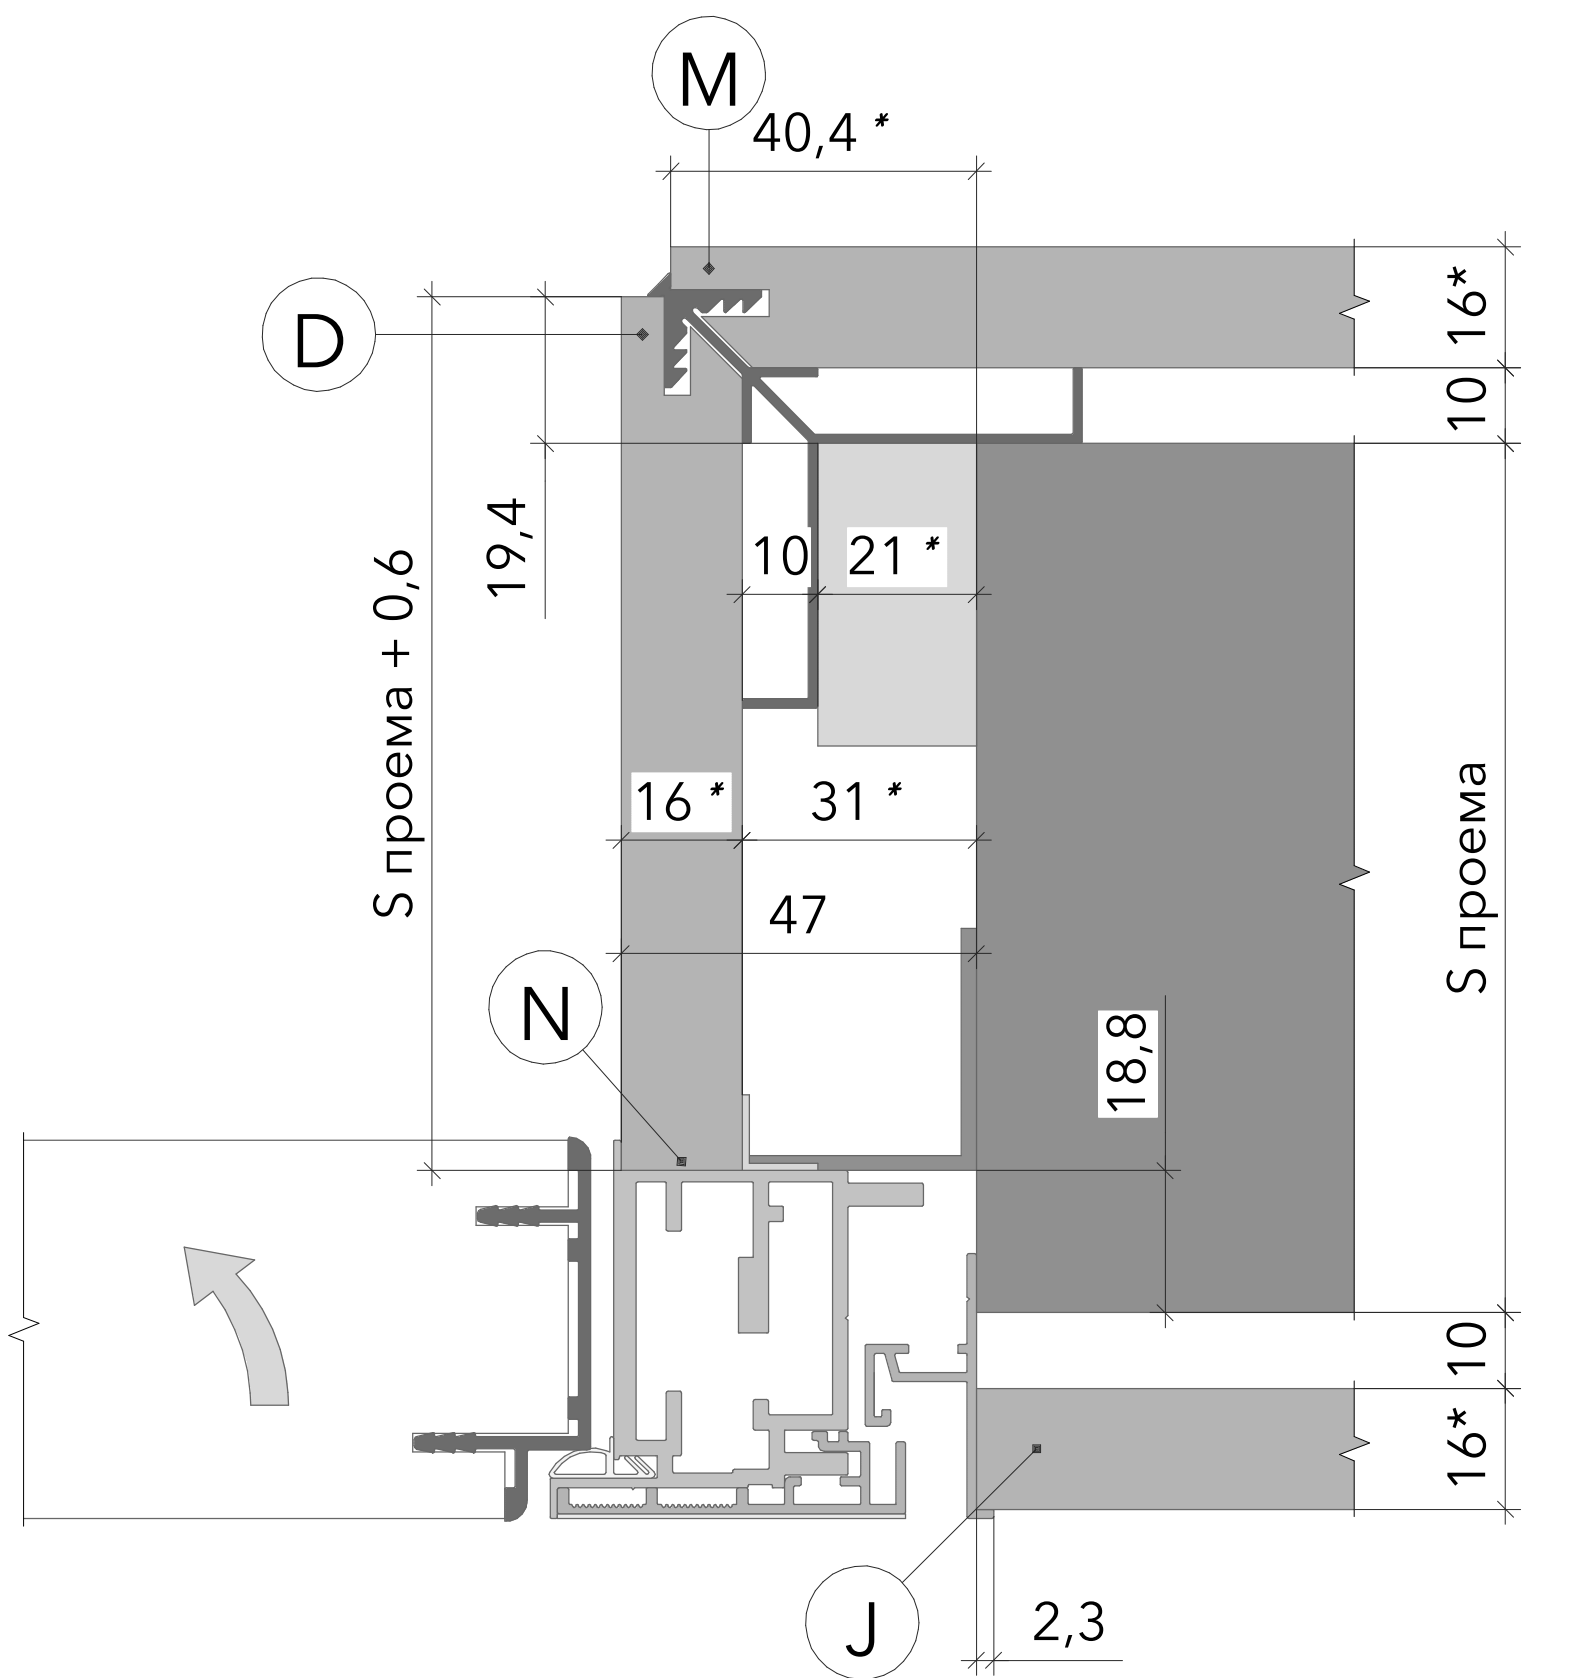

* - Толщина панели зависит от варианта отделки.