



Узлы стеновых панелей. Complanar 50 теневая коробка.


J
Теневая коробка Complanar
Открытие наружу
Конфигурация проема. Тип 1

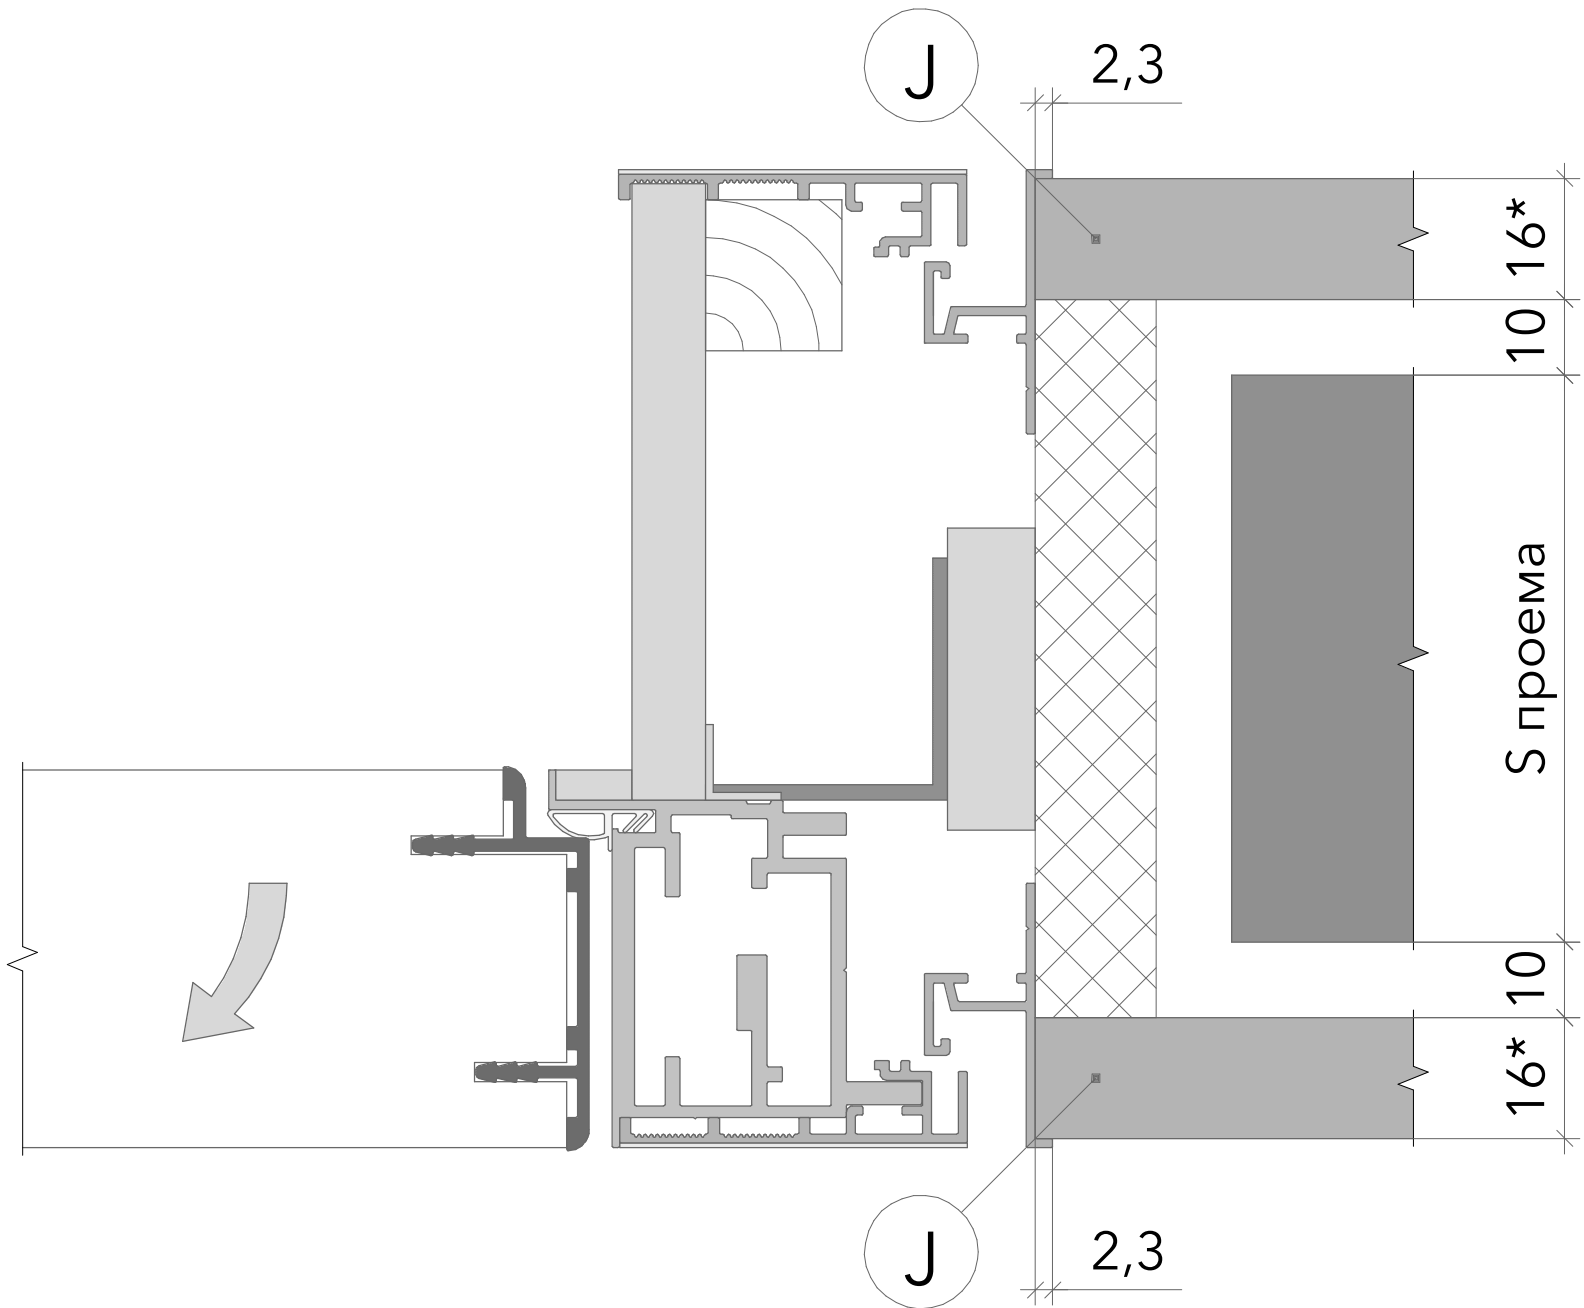


J
Теневая коробка Complanar
Открытие наружу
Конфигурация проема. Тип 2

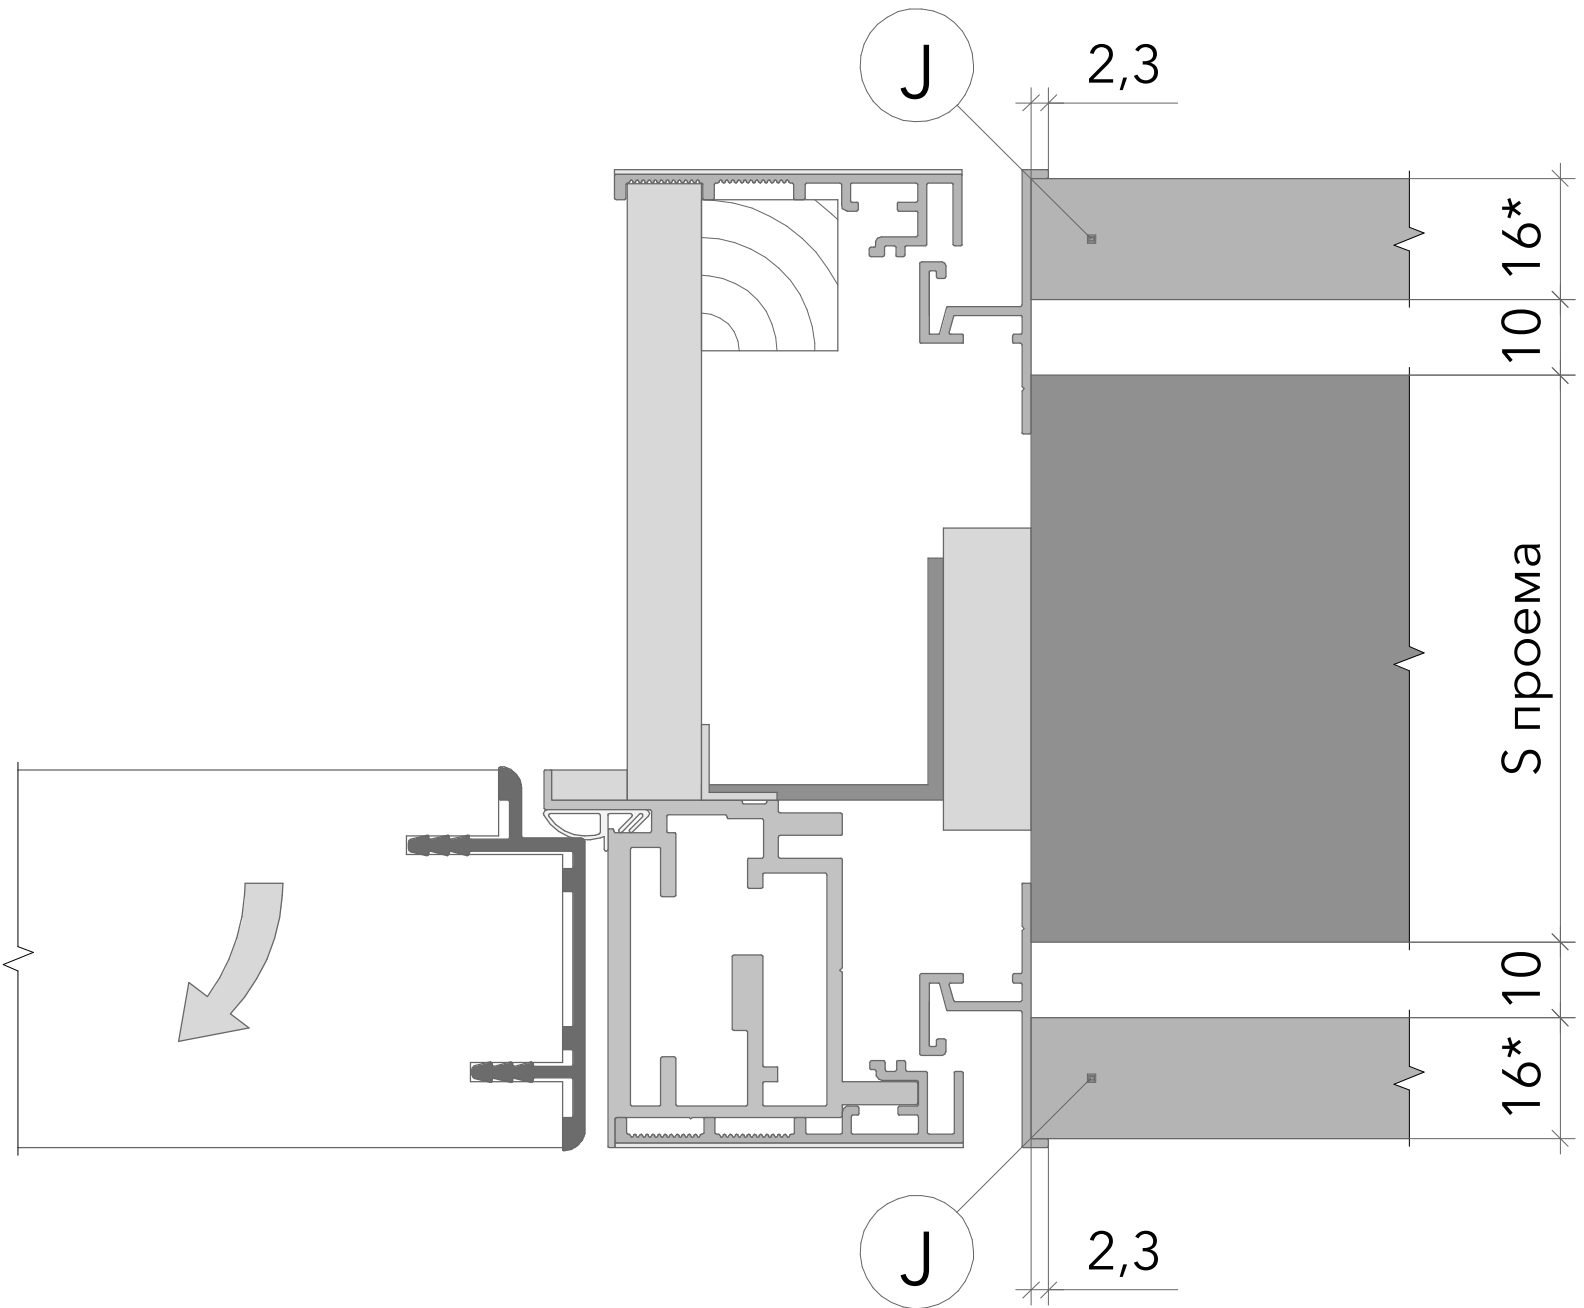


K
Теневой плинтус

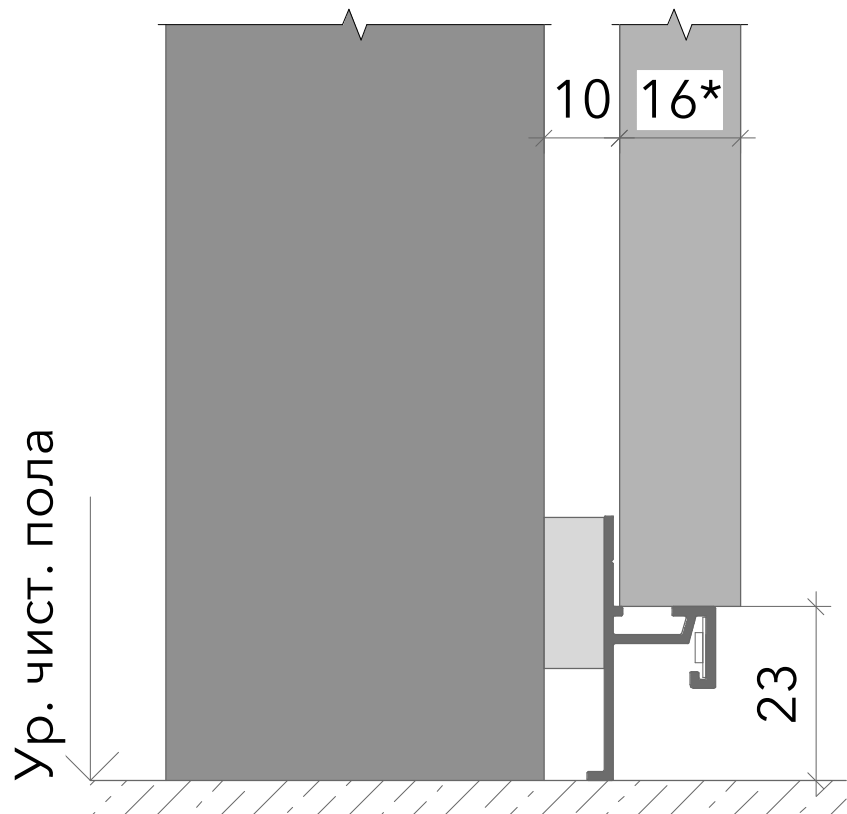

J
Теневая коробка Complanar
Открытие внутрь
Конфигурация проема. Тип 1

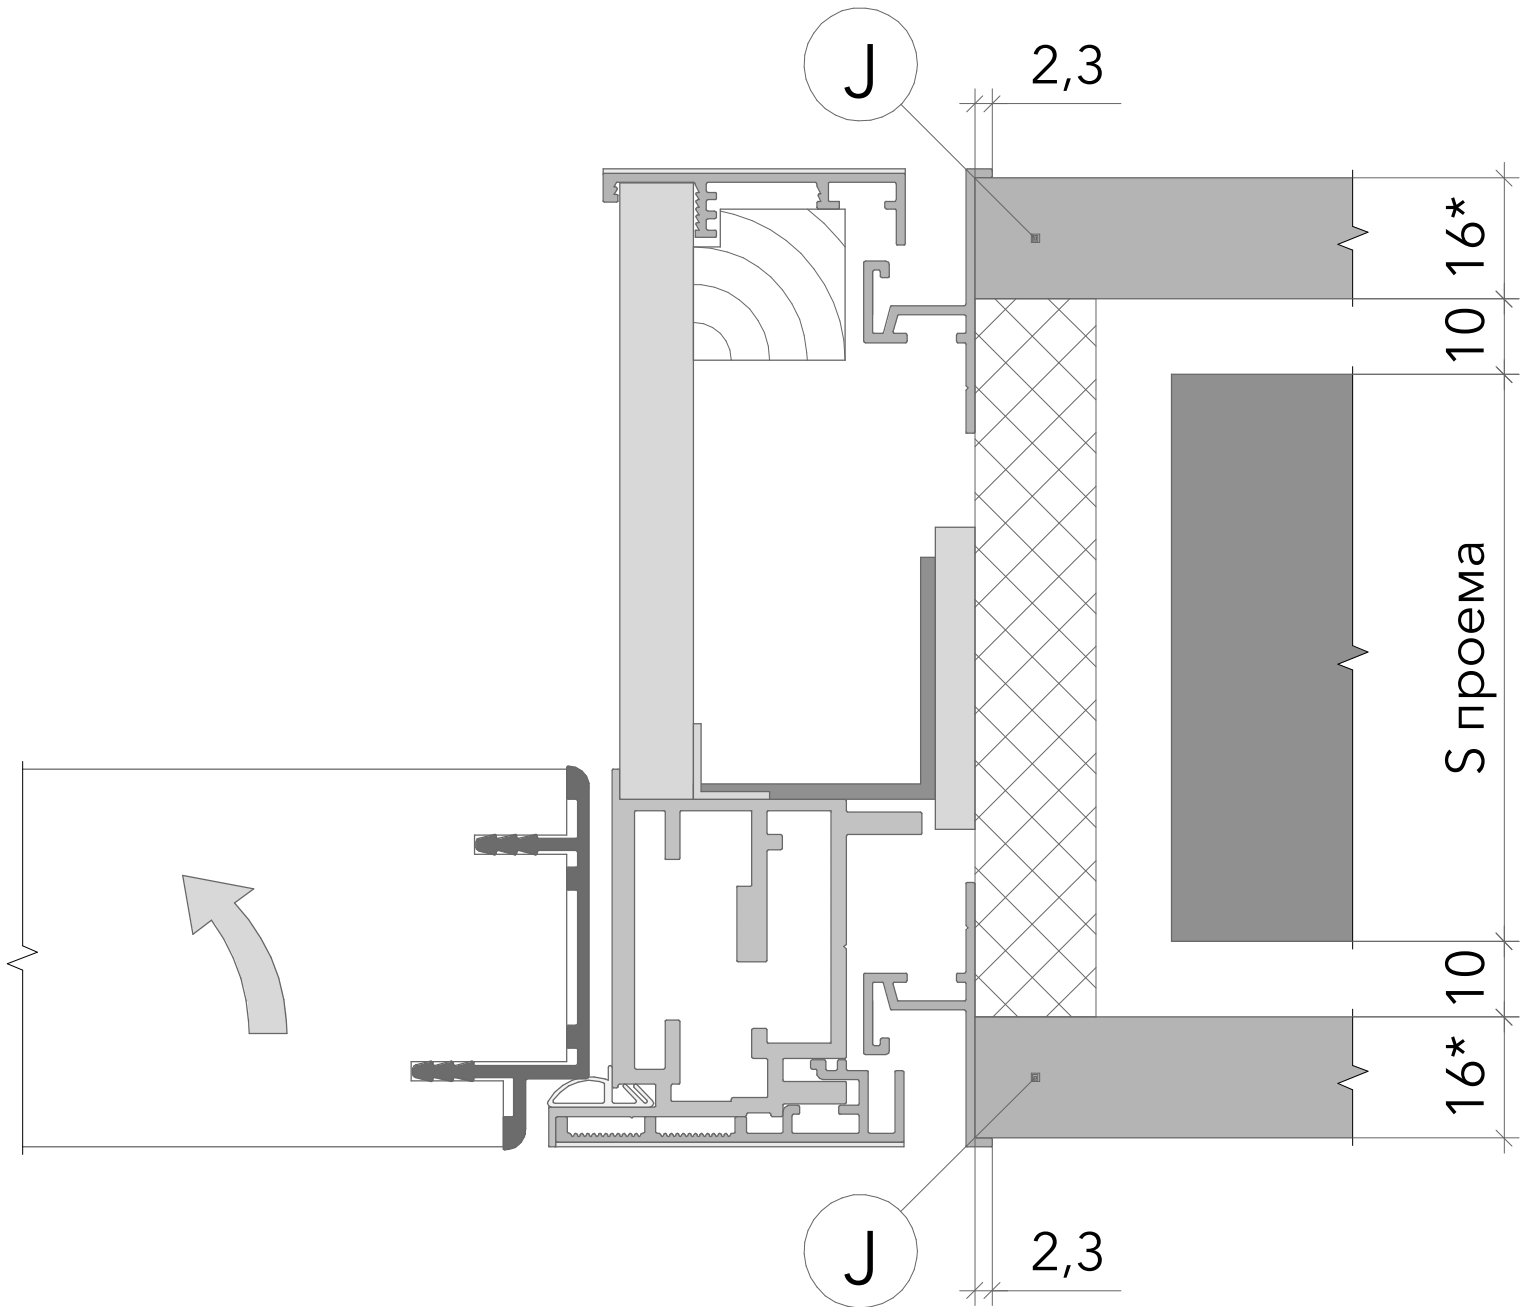

J
Теневая коробка Complanar
Открытие внутрь
Конфигурация проема. Тип 2

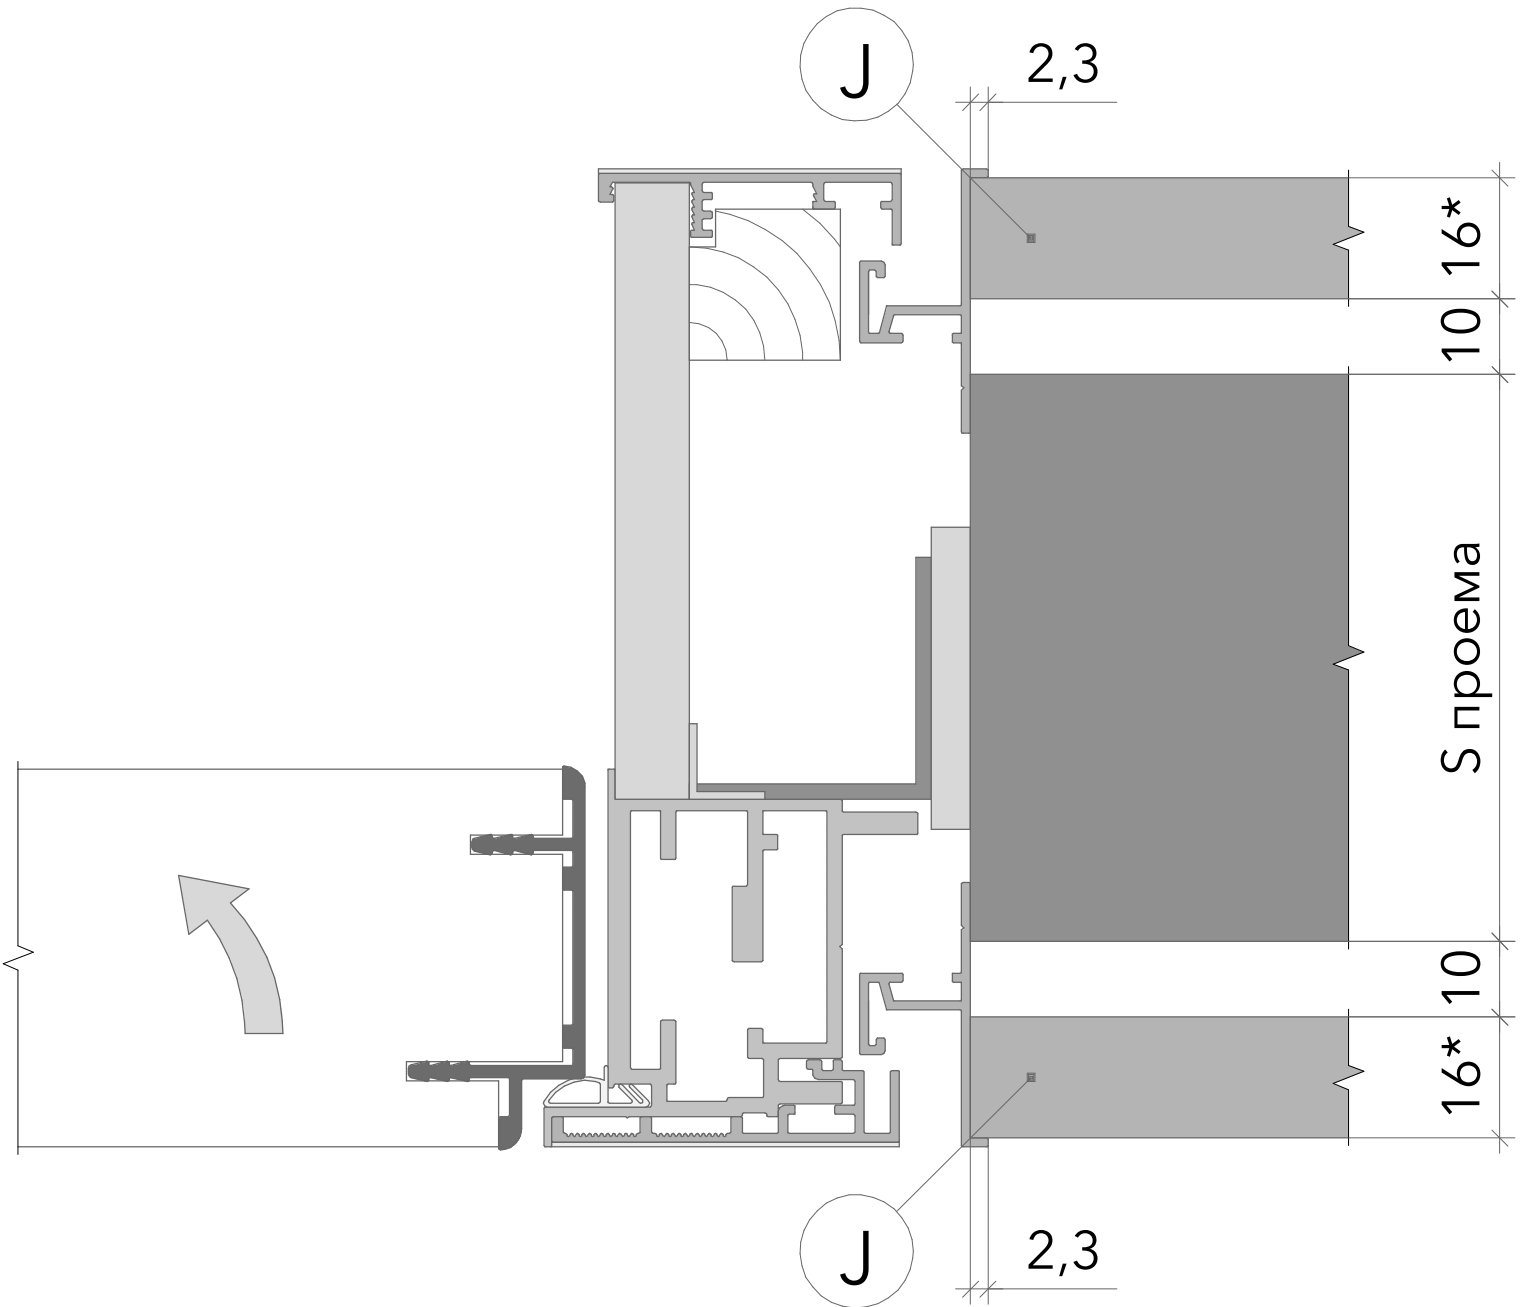

* - Толщина панели зависит от варианта отделки.